

**NOTE:**

- (0.1) THE DRAWING IS THE COPYRIGHT OF THE ARCHITECTS AND IS NOT BE PRODUCED COPIED HANDED OVER TO THE THIRD PARTY OR USED FOR ANY OTHER PURPOSE OTHER THAN FOR WHICH IT IS HANDED.
- (0.2) ALL DIMENSIONS SHALL BE COUNTED CHECKED ON THE SITE PRIOR TO START OF WORK.
- (0.3) WRITTEN DIMENSIONS SHOULD BE FOLLOWED.
- (0.4) ANY CHANGE REQUIRED SHALL BE CONFIRMED FROM THE ARCHITECT.
- (0.5) THIS DRAWING SHALL BE READ IN CONJUNCTION WITH OTHER PERTINENT DRAWINGS.

**LEGEND:**

**DRAWING REVISIONS**

REV	DESCRIPTION	DATE	DRAWN	CHKD

**DRAWING ISSUED FOR :**

<input checked="" type="radio"/>	APPROVAL
<input type="radio"/>	GOOD FOR CONSTRUCTION
<input type="radio"/>	SUBMISSION
<input type="radio"/>	AS BUILT

**PROJECT:**

# PROPOSED OFFICE AUTOMAT

**CLIENT:**

**SIDHARTH AUTOTECH**

**AUTOMAT**



**INDIA PVT. LTD.**

**SLS** SLS Designs India Pvt. Ltd  
507, 5th Floor, Time Tower  
MG Road, Gurugram  
Haryana -122002, India.  
Ph:+91-124-4108106,4035926  
Email: info@sldesigns.in  
website: www.sldesigns.in

**DRAWING TITLE:**  
**PROPOSED PLAN GROUND AND FIRST FLOOR**

DRAWING NO.- AUT/RAJ/GF/FF/101

DRAWN BY:	DATE:	NORTH:
RG	22-05-25	
CHECKED BY:	SCALE:	
GS	NTS	
APPROVED BY:	REV. NO.:	
GS	R3	

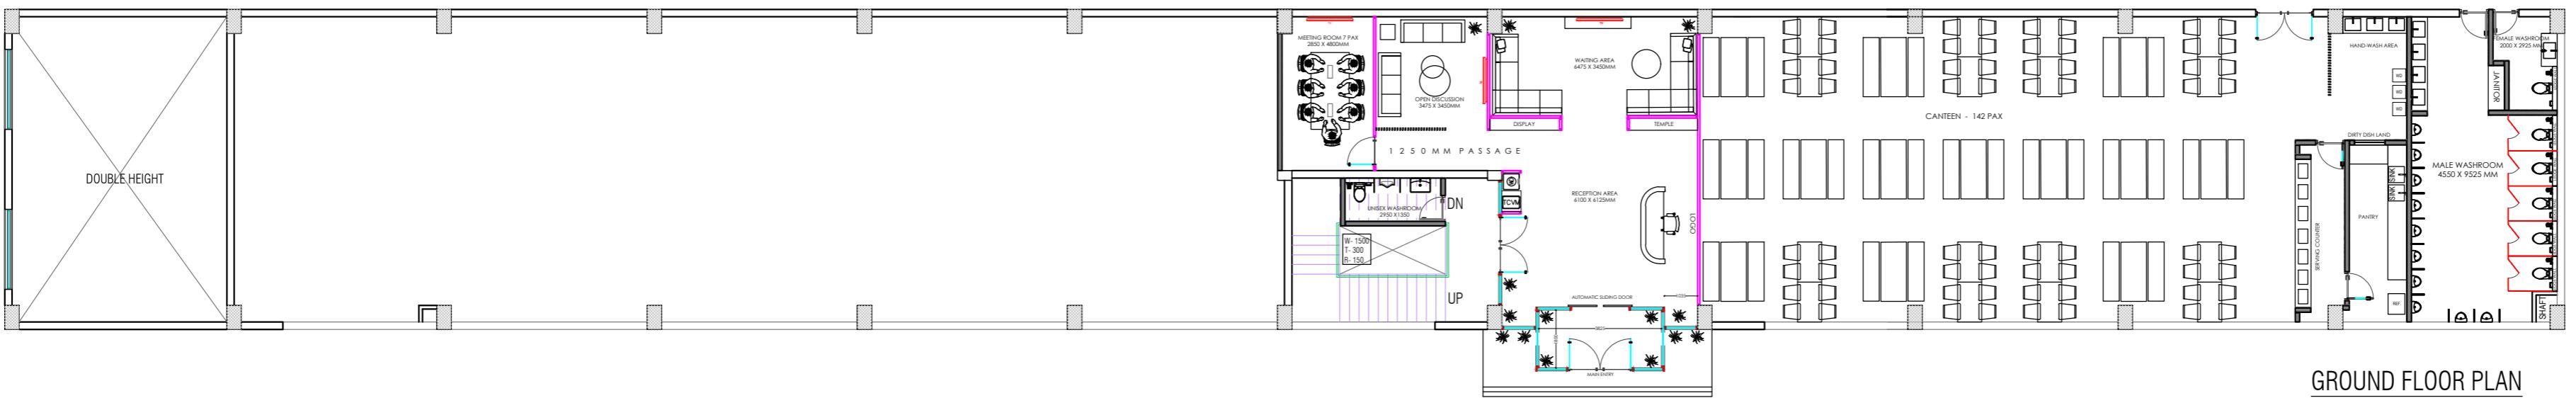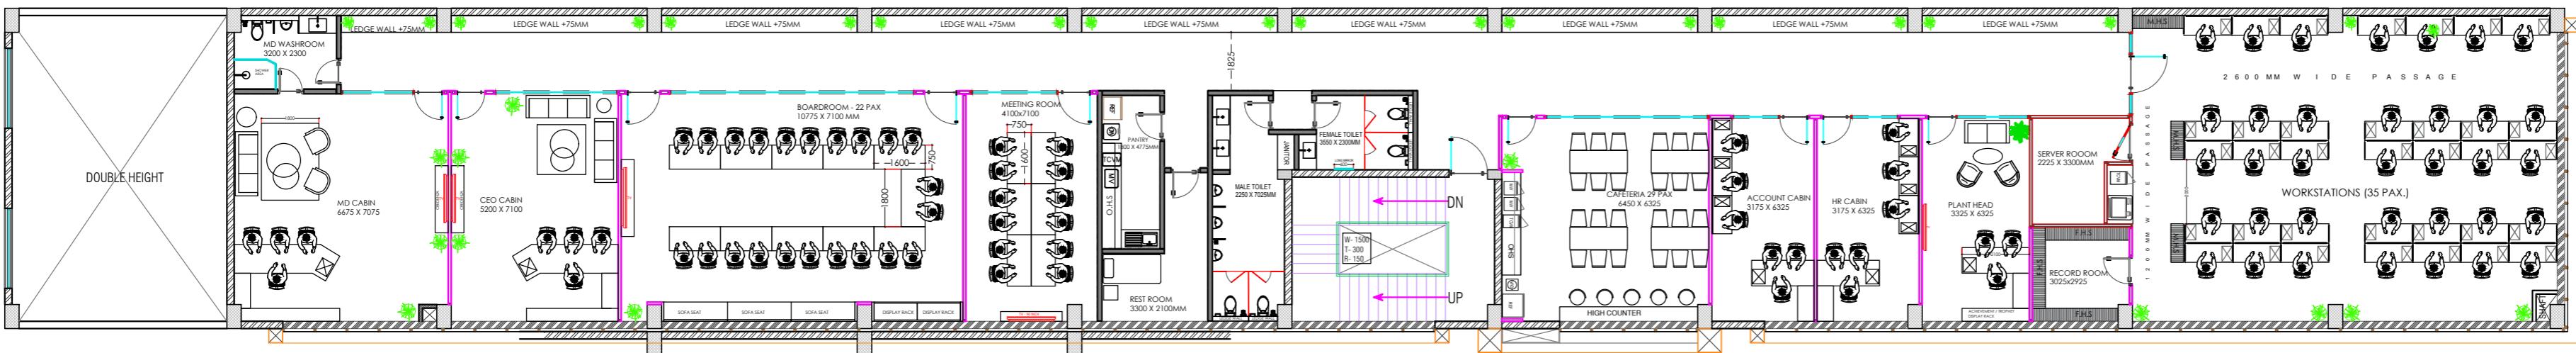

**GROUND FLOOR**

OCCUPANCY CHART			
S.NO.	DESCRIPTION	REQUIRED	ACHIEVED
1	RECEPTION / WAITING	01	01
2	CANTEEN	150 PAX	142 PAX
3	MEETING ROOM-07 PAX	01	01
4	OPEN DISCUSSION	00	01
5	UNISEX WASHROOM	01	01
6	MALE TOILET	01	01
7	FEMALE TOILET	01	01

**FIRST FLOOR**

OCCUPANCY CHART			
S.NO.	DESCRIPTION	REQUIRED	ACHIEVED
1	CAFETERIA - 29 PAX	01	01
2	BOARD ROOM-22 + 09	01	01
3	MEETING ROOM - 12 PAX	01	01
4	REST ROOM	01	01
5	WORKSTATION (1500X1500)	25-30	35
6	SERVER ROOM	01	01
7	RECORD ROOM	01	01
8	PLANT HEAD	01	01
9	HR CABIN 3+1 SENIOR	01	01
10	ACCOUNT ROOM 3+1 SENIOR	01	01
11	MD CABIN	01	01
12	CEO CABIN	01	01
13	MD CABIN WASHROOM	01	01
15	PANTRY	02	02
16	MALE TOILET	01	01
17	FEMALE TOILET	01	01
18	REPRO COUNTER	01	01

**APPROVED**

27-MAY-2025

For Sidharth Automat India Pvt. Ltd.

  
Authorised Signatory